


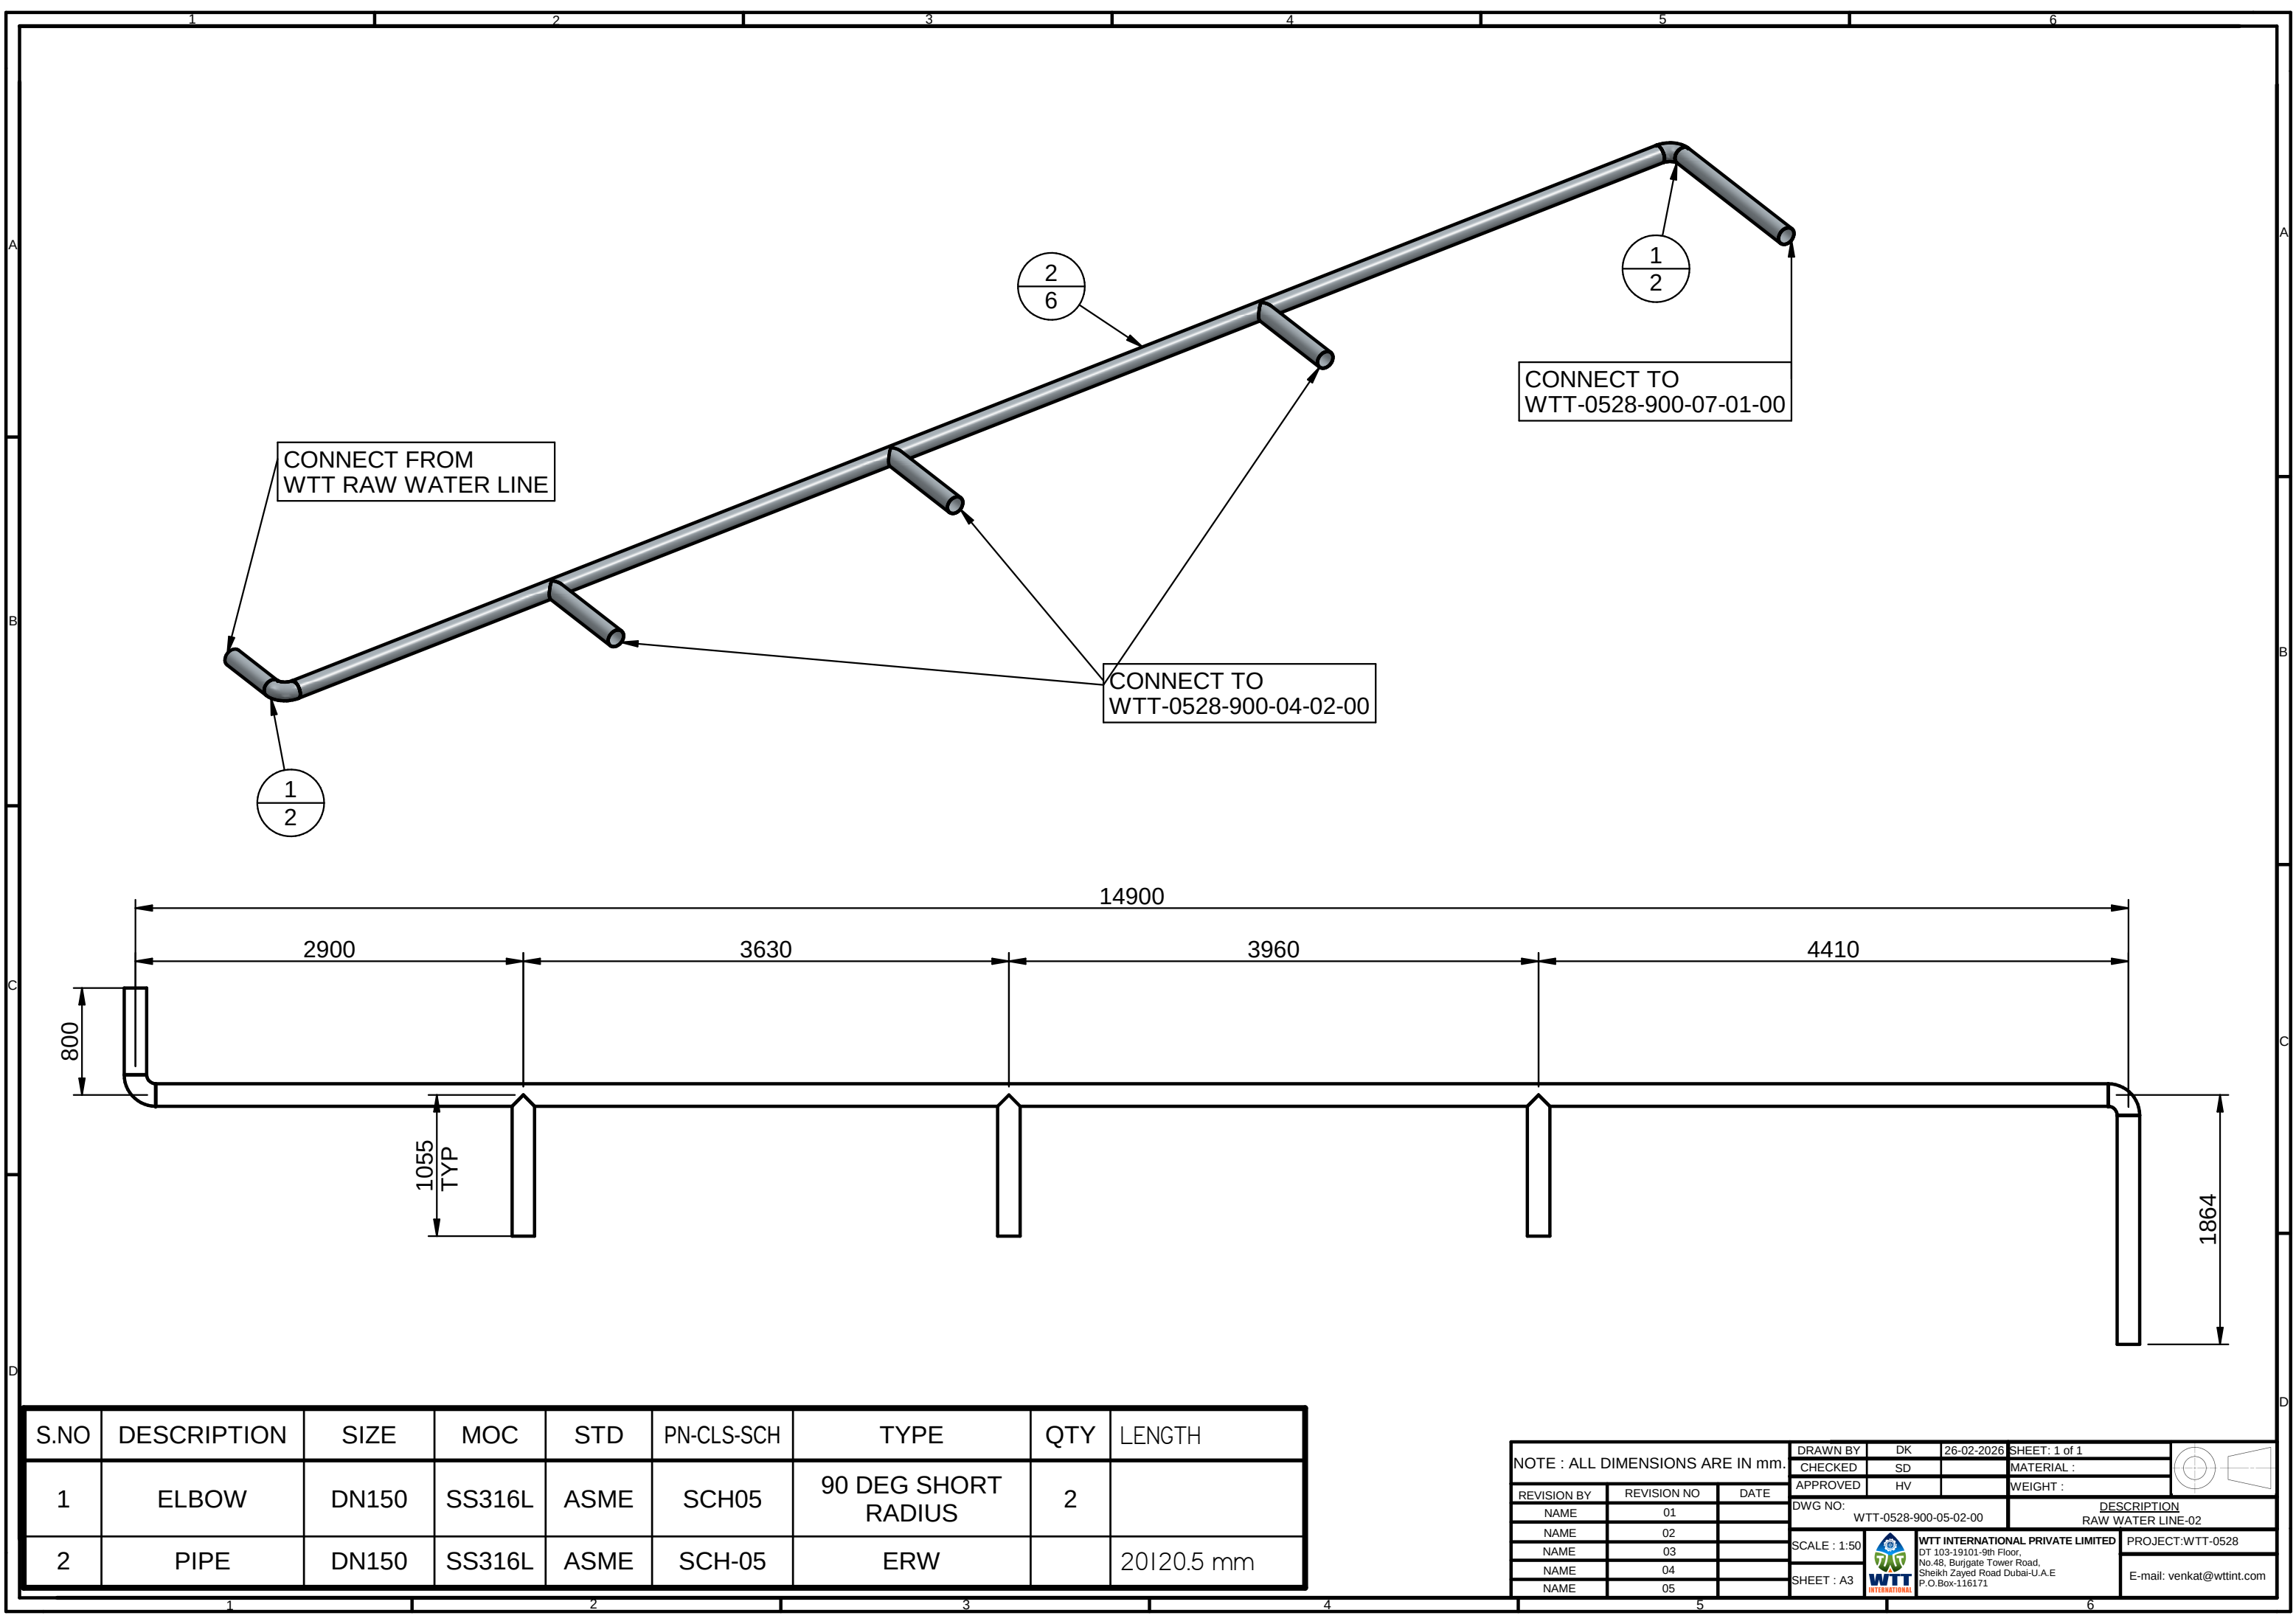

S.NO	DESCRIPTION	SIZE	MOC	STD	PN-CLS-SCH	TYPE	QTY	LENGTH
1	ELBOW	DN150	SS316L	ASME	SCH05	90 DEG SHORT RADIUS	2	
2	PIPE	DN150	SS316L	ASME	SCH-05	ERW		20 20.5 mm

NOTE : ALL DIMENSIONS ARE IN mm.			DRAWN BY	DK	26-02-2026	SHEET: 1 of 1	
			CHECKED	SD			
			APPROVED	HV		WEIGHT :	
			DWG NO: WTT-0528-900-05-02-00			DESCRIPTION RAW WATER LINE-02	
			SCALE : 1:50			PROJECT:WTT-0528	
			SHEET : A3			E-mail: venkat@wttint.com	
						WTT INTERNATIONAL PRIVATE LIMITED DT 103-19101-9th Floor, No.48, Burigate Tower Road, Sheikh Zayed Road Dubai-U.A.E P.O.Box-116171	